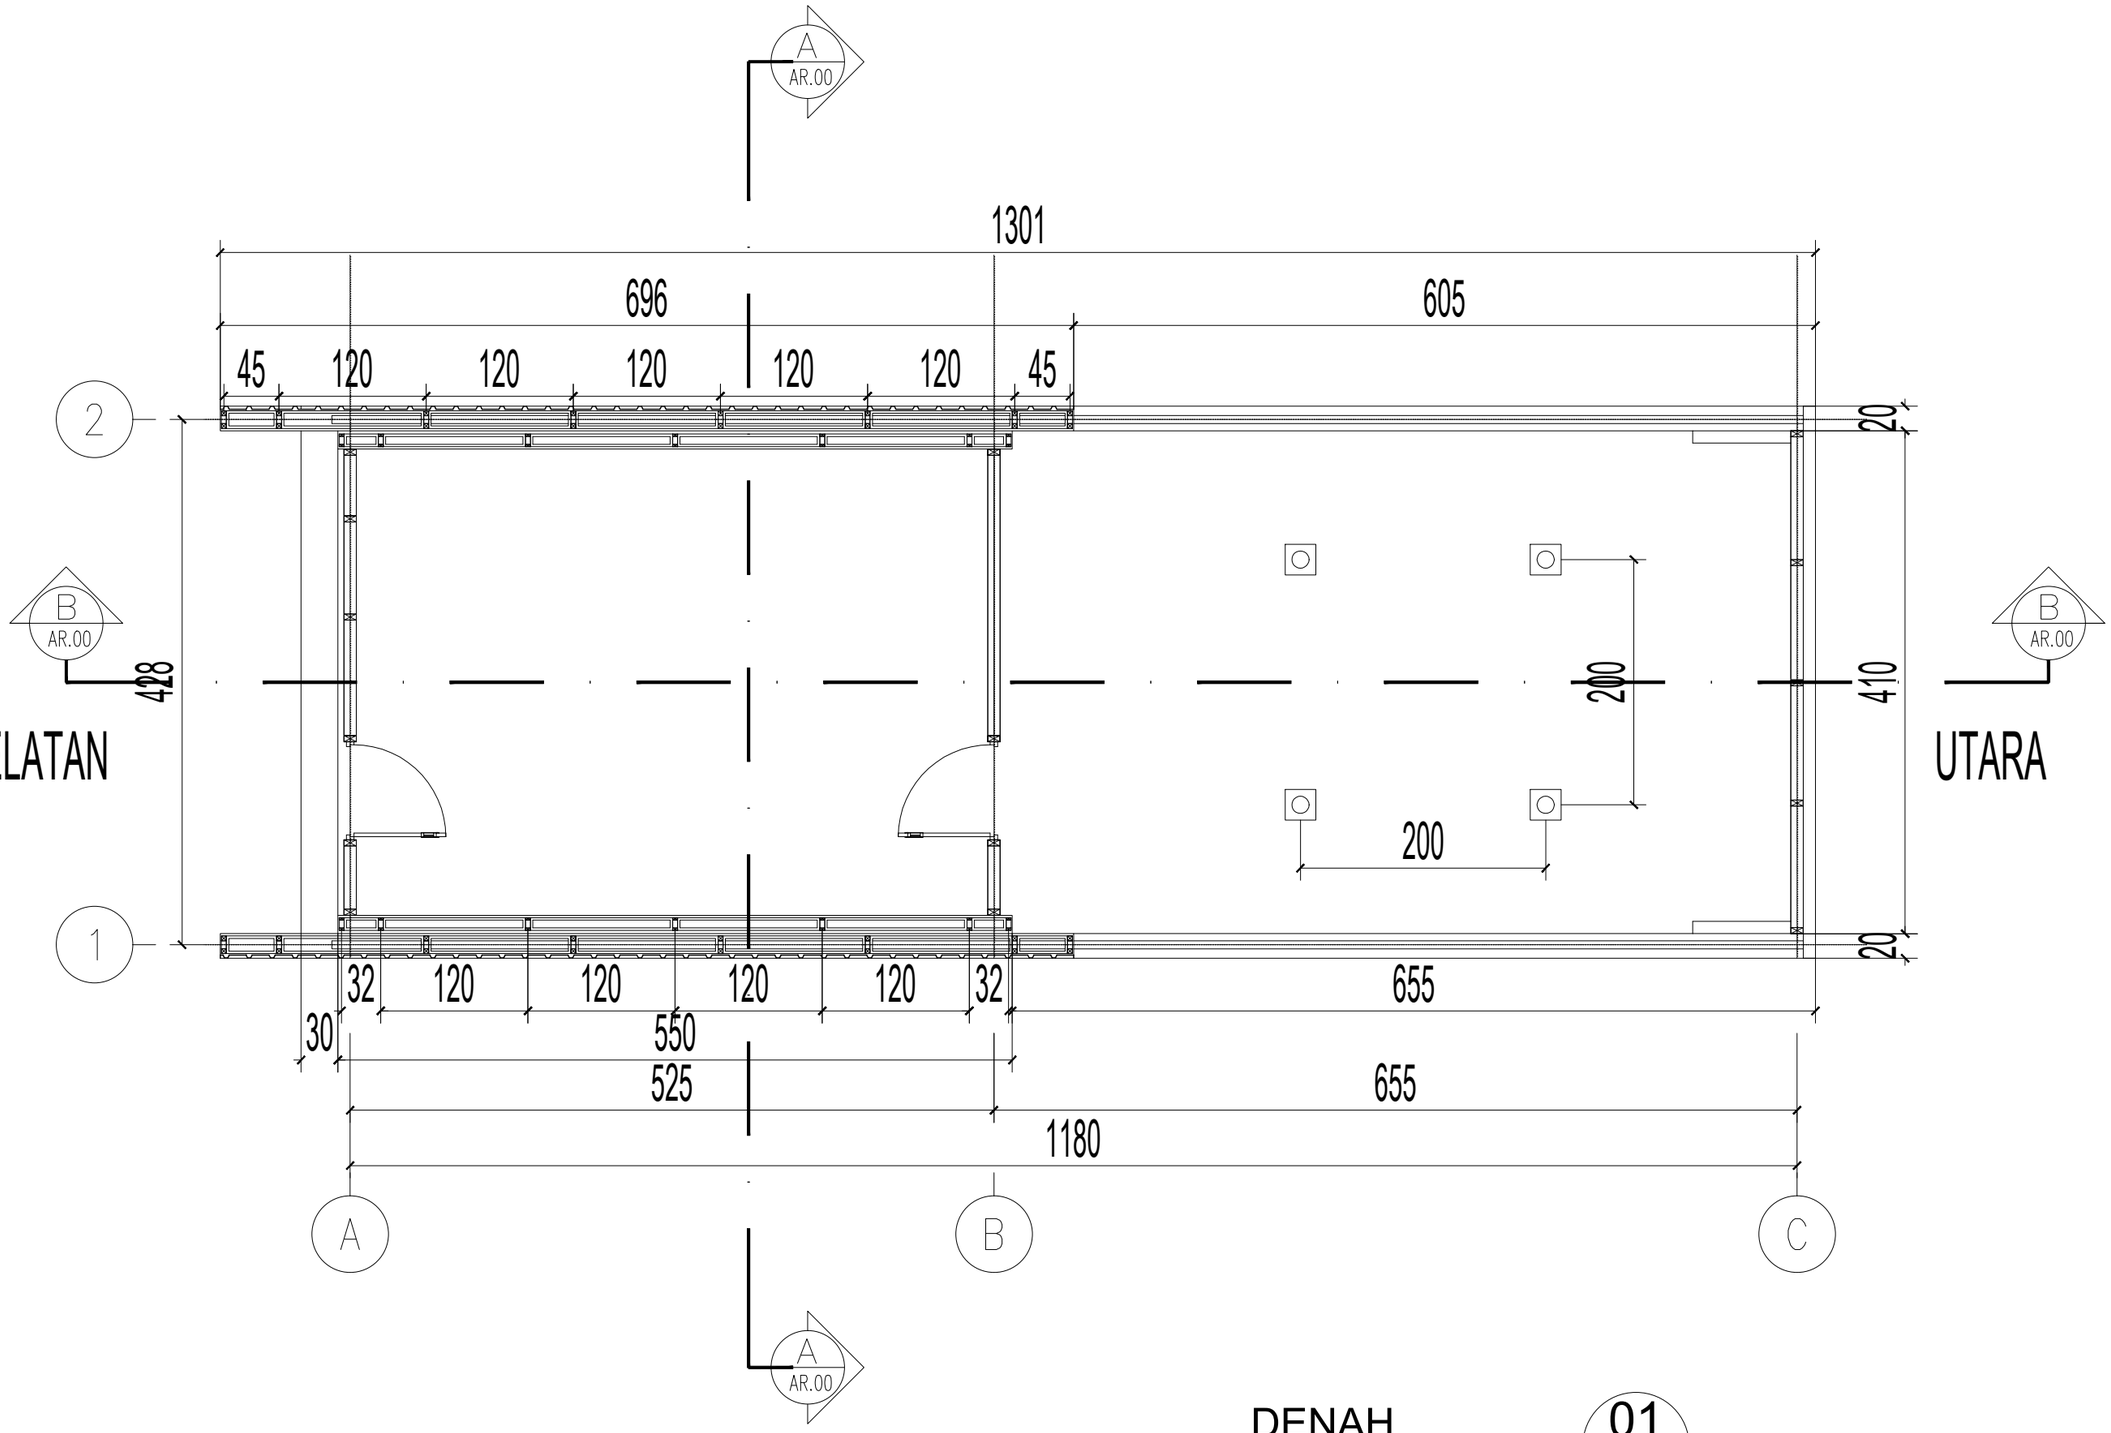


DENAH

SKALA 1 : 50

01
- AR-01

PEMBERI KERJA

CATATAN

REVISI

No.	Rincian	Tanggal	Paraf

PEKERJAAN

DED
OBSERVATORY ROOM

DISETUJUI OLEH

-

-
-

KONSULTAN PERENCANA

PENANGGUNG JAWAB

-
Direktur Utama


TEAM LEADER

-
Team Leader

JUDUL GAMBAR

DENAH

SKALA	TANGGAL	NO.LEMBAR
1 : 50	2026	AR-27

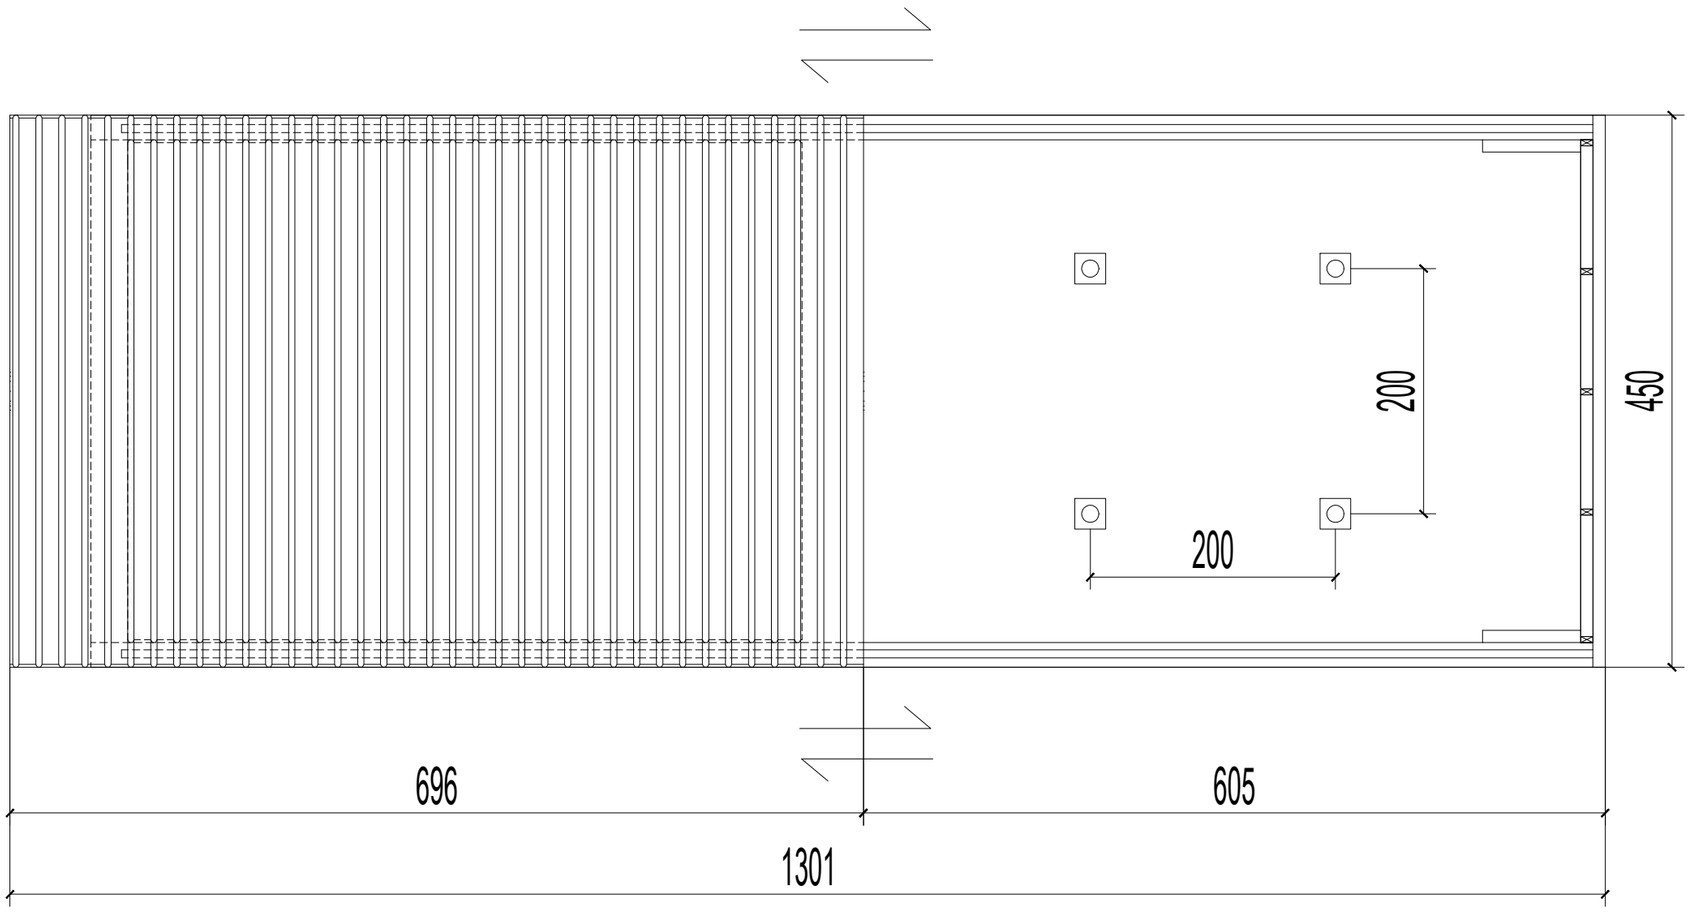

DENAH ATAP TERBUKA

SKALA 1 : 50

01
- AR-01

PEMBERI KERJA

CATATAN

REVISI

No.	Rincian	Tanggal	Paraf

PEKERJAAN

DED
OBSERVATORY ROOM

DISETUJUI OLEH

-

-
-

KONSULTAN PERENCANA

PENANGGUNG JAWAB

-
Direktur Utama


TEAM LEADER

-
Team Leader

JUDUL GAMBAR

DENAH ATAP TERBUKA

SKALA	TANGGAL	NO.LEMBAR
1 : 50	2026	AR-27

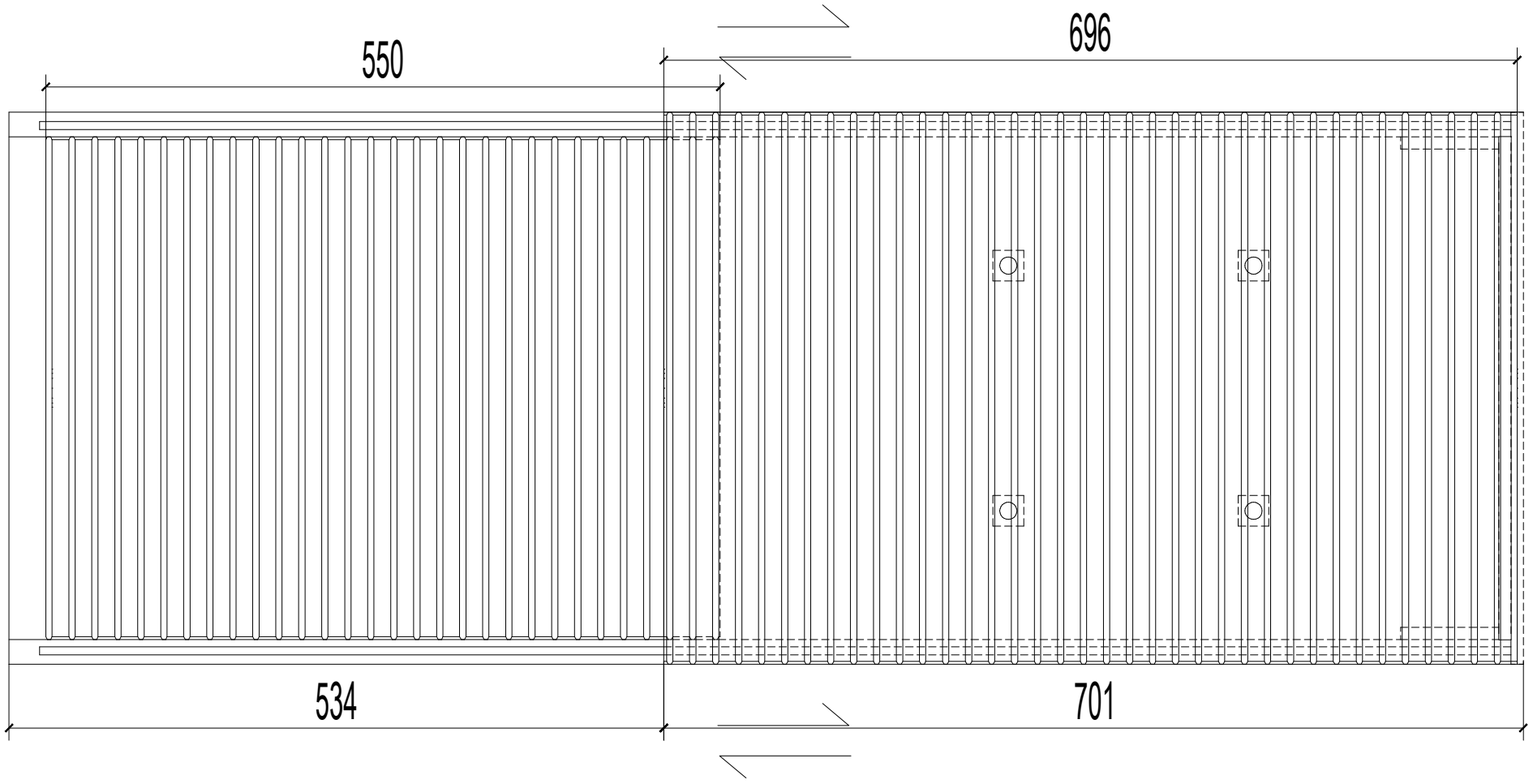

DENAH ATAP TERTUTUP 01

SKALA 1 : 50

-
AR-01

PEMBERI KERJA

CATATAN

REVISI

No.	Rincian	Tanggal	Paraf

PEKERJAAN

DED

OBSERVATORY ROOM

DISETUJUI OLEH

-

-

-

KONSULTAN PERENCANA

PENANGGUNG JAWAB

-

Direktur Utama

TEAM LEADER


-

Team Leader

JUDUL GAMBAR

DENAH ATAP TERTUTUP


SKALA	TANGGAL	NO.LEMBAR
1 : 50	2026	AR-27

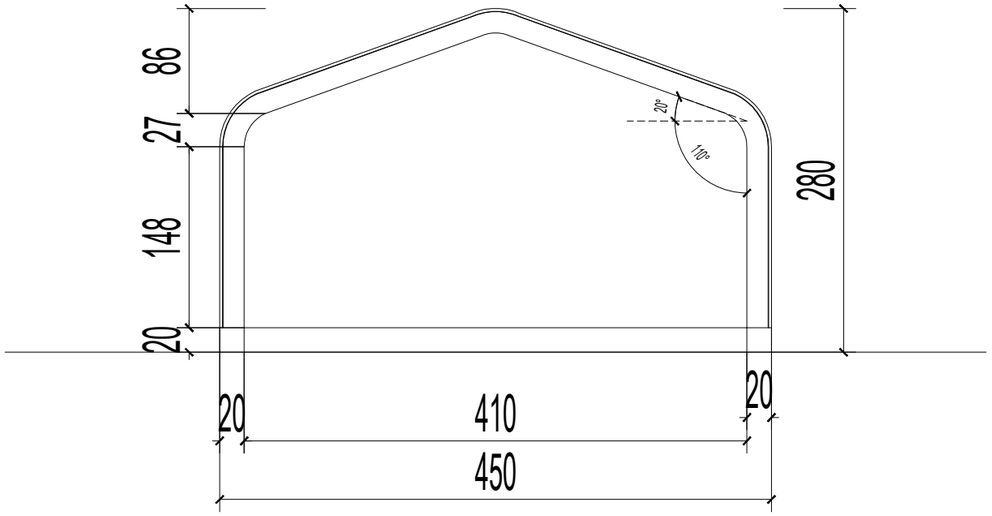

TAMPAK UTARA

SKALA 1 : 50

01 | - | AR-01

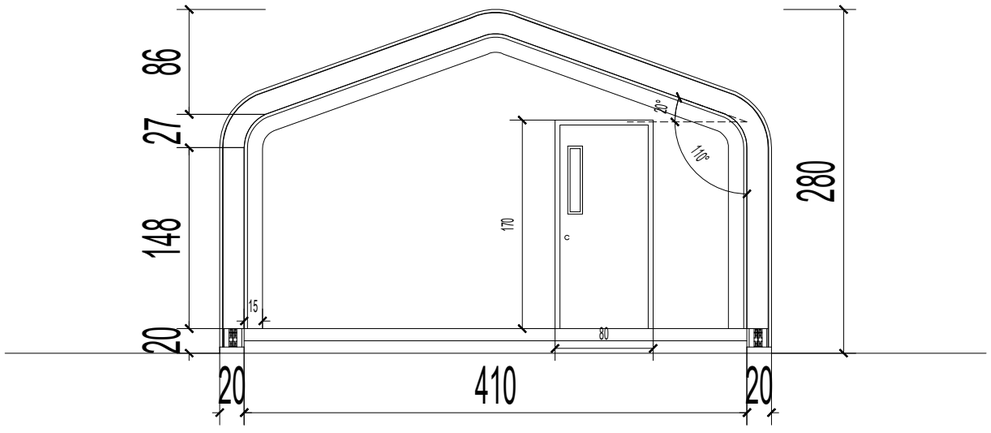

TAMPAK SELATAN

SKALA 1 : 50

01 | - | AR-01

PEMBERI KERJA

CATATAN

REVISI

No.	Rincian	Tanggal	Paraf

PEKERJAAN

DED

OBSERVATORY ROOM

DISETUJUI OLEH

-

-

-

KONSULTAN PERENCANA

PENANGGUNG JAWAB

-

Direktur Utama

TEAM LEADER


-

Team Leader

JUDUL GAMBAR

TAMPAK SELATAN

SKALA	TANGGAL	NO.LEMBAR
1 : 50	2026	AR-27

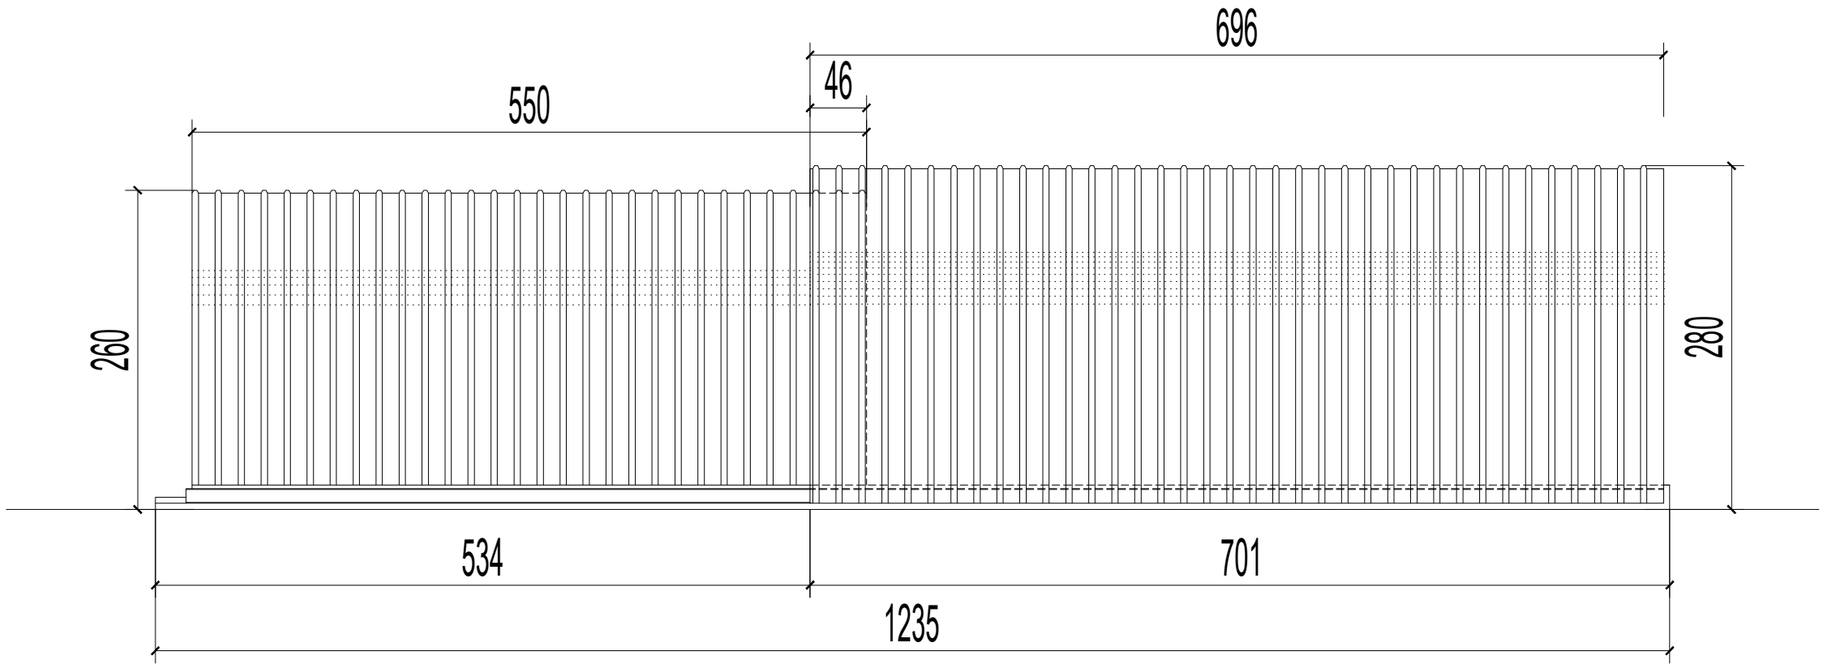

TAMPAK TIMUR

SKALA 1 : 50

01
- | AR-01

PEMBERI KERJA

CATATAN

REVISI

No.	Rincian	Tanggal	Paraf

PEKERJAAN

DED
OBSERVATORY ROOM

DISETUJUI OLEH

-

-
-

KONSULTAN PERENCANA

PENANGGUNG JAWAB

-
Direktur Utama


TEAM LEADER

-
Team Leader

JUDUL GAMBAR

TAMPAK TIMUR

SKALA	TANGGAL	NO.LEMBAR
1 : 50	2026	AR-27

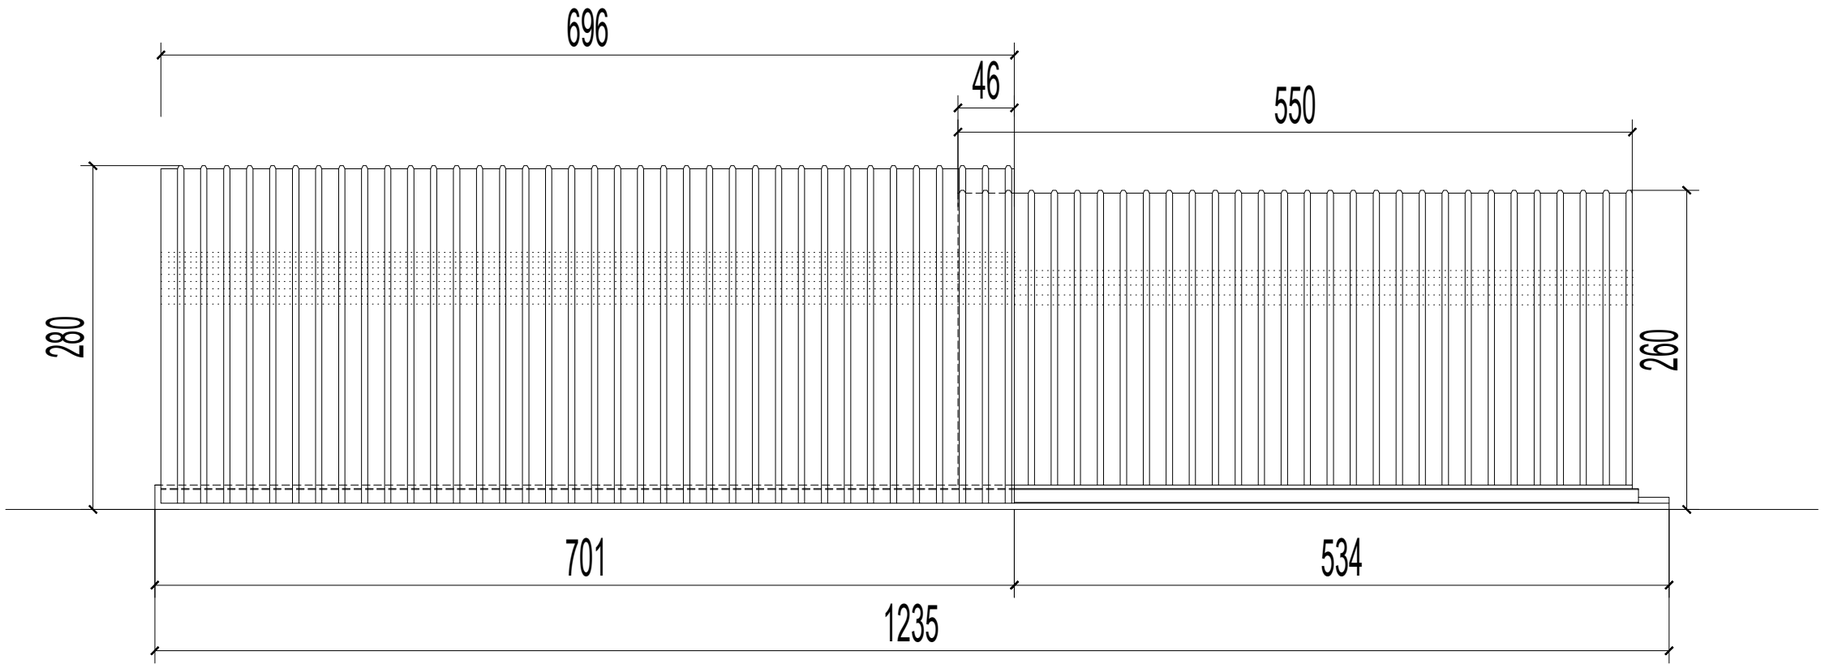

TAMPAK BARAT

SKALA 1 : 50

01 | AR-01

PEMBERI KERJA

CATATAN

REVISI

No.	Rincian	Tanggal	Paraf

PEKERJAAN

DED
OBSERVATORY ROOM

DISETUJUI OLEH

-

-
-

KONSULTAN PERENCANA

PENANGGUNG JAWAB

-
Direktur Utama


TEAM LEADER

-
Team Leader

JUDUL GAMBAR

TAMPAK BARAT

SKALA	TANGGAL	NO.LEMBAR
1 : 50	2026	AR-27

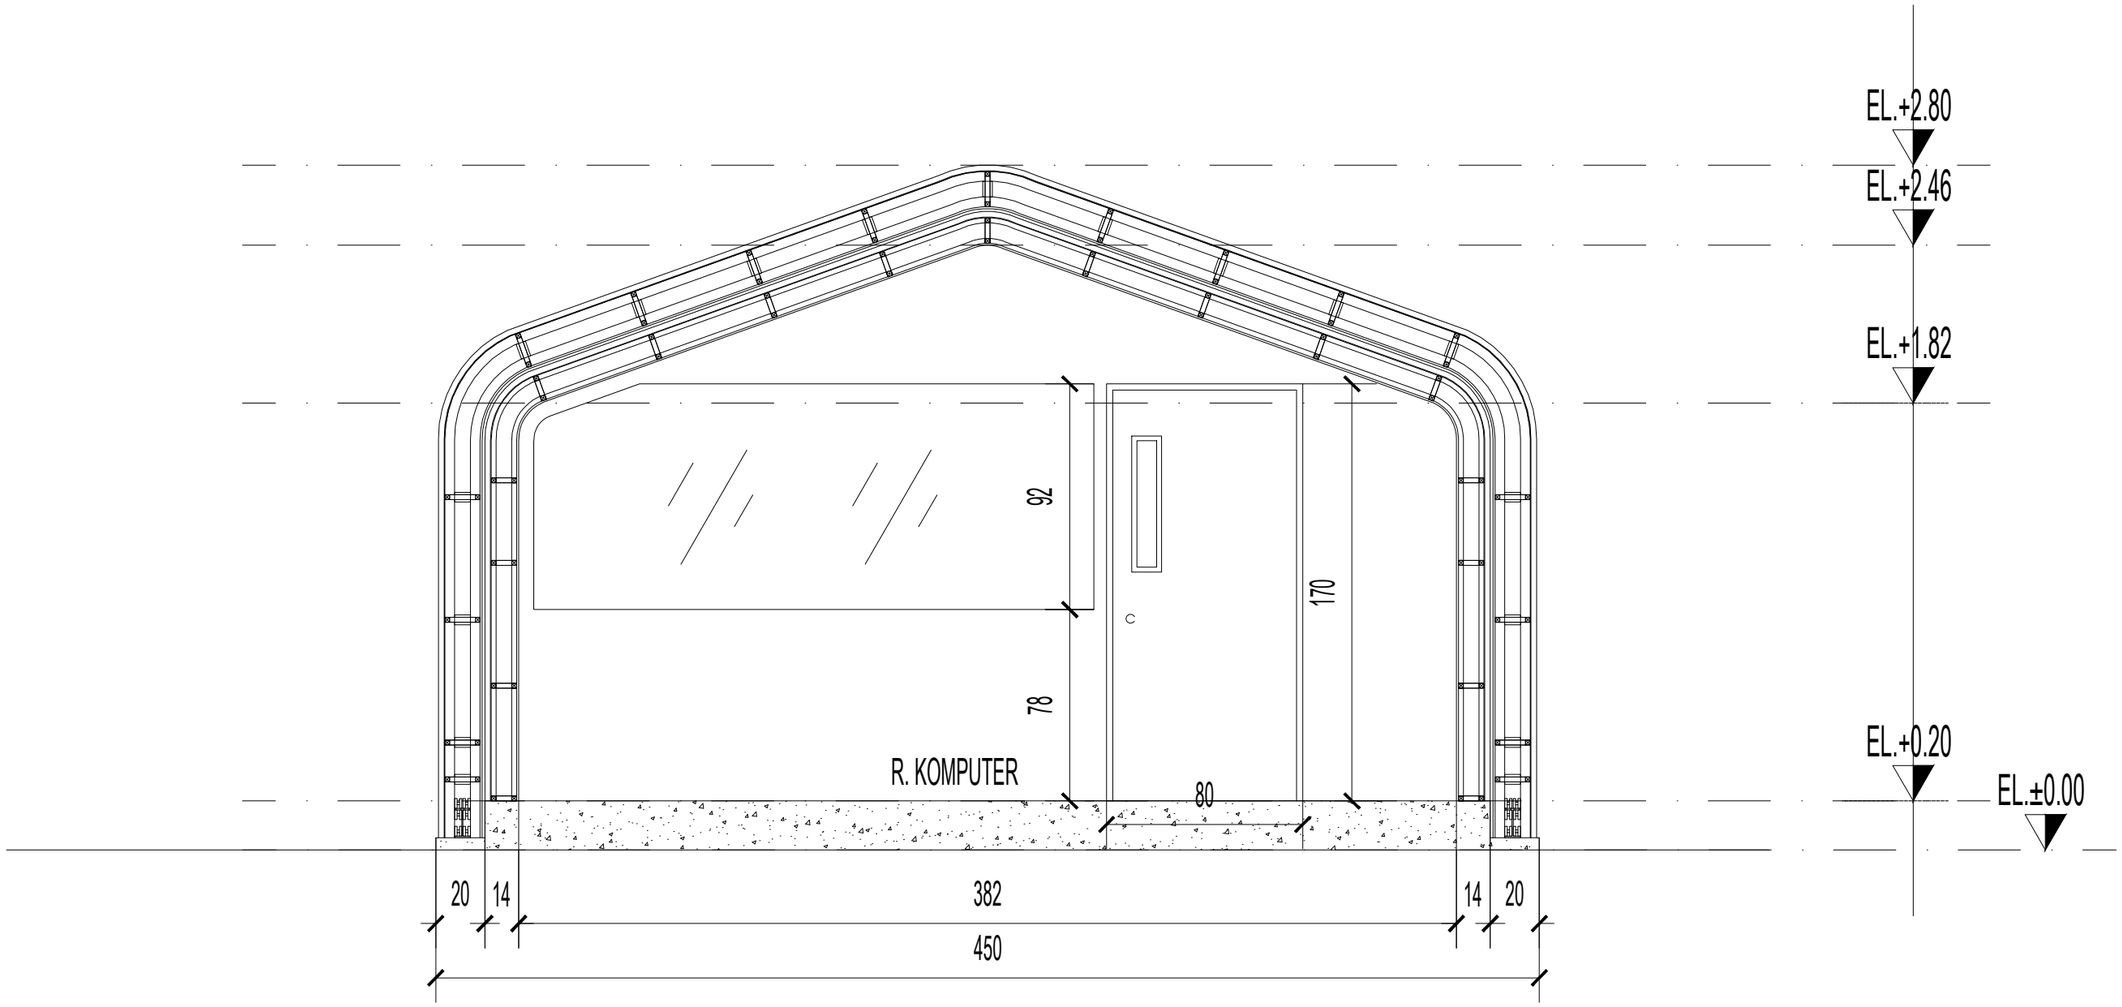

POTONGAN A-A

SKALA 1 : 25

01
- AR-01

PEMBERI KERJA

CATATAN

REVISI

No.	Rincian	Tanggal	Paraf

PEKERJAAN

DED
OBSERVATORY ROOM

DISETUJUI OLEH

-

-
-

KONSULTAN PERENCANA

PENANGGUNG JAWAB

-
Direktur Utama


TEAM LEADER

-
Team Leader

JUDUL GAMBAR

POTONGAN A-A

SKALA	TANGGAL	NO.LEMBAR
1 : 25	2026	AR-27

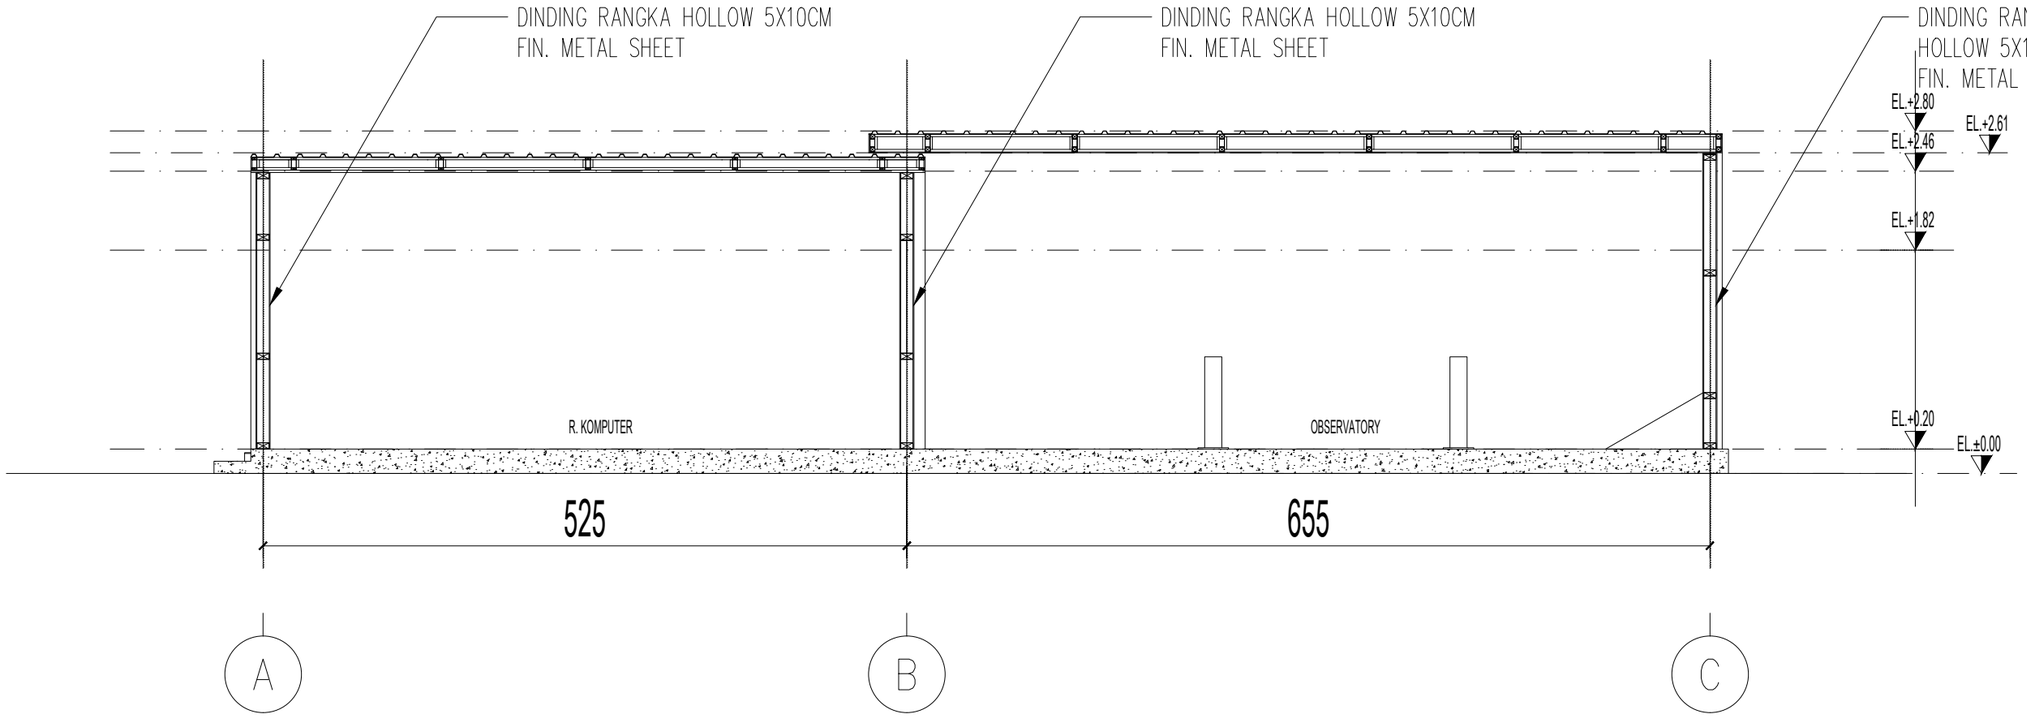

POTONGAN B-B

SKALA 1 : 50

01

\- | AR-01

PEMBERI KERJA

CATATAN

REVISI

No.	Rincian	Tanggal	Paraf

PEKERJAAN

DED

OBSERVATORY ROOM

DISETUJUI OLEH

\-

\-

\-

KONSULTAN PERENCANA

PENANGGUNG JAWAB

\-

Direktur Utama

TEAM LEADER


\-

Team Leader

JUDUL GAMBAR

POTONGAN B-B

SKALA	TANGGAL	NO.LEMBAR
1 : 50	2026	AR-27

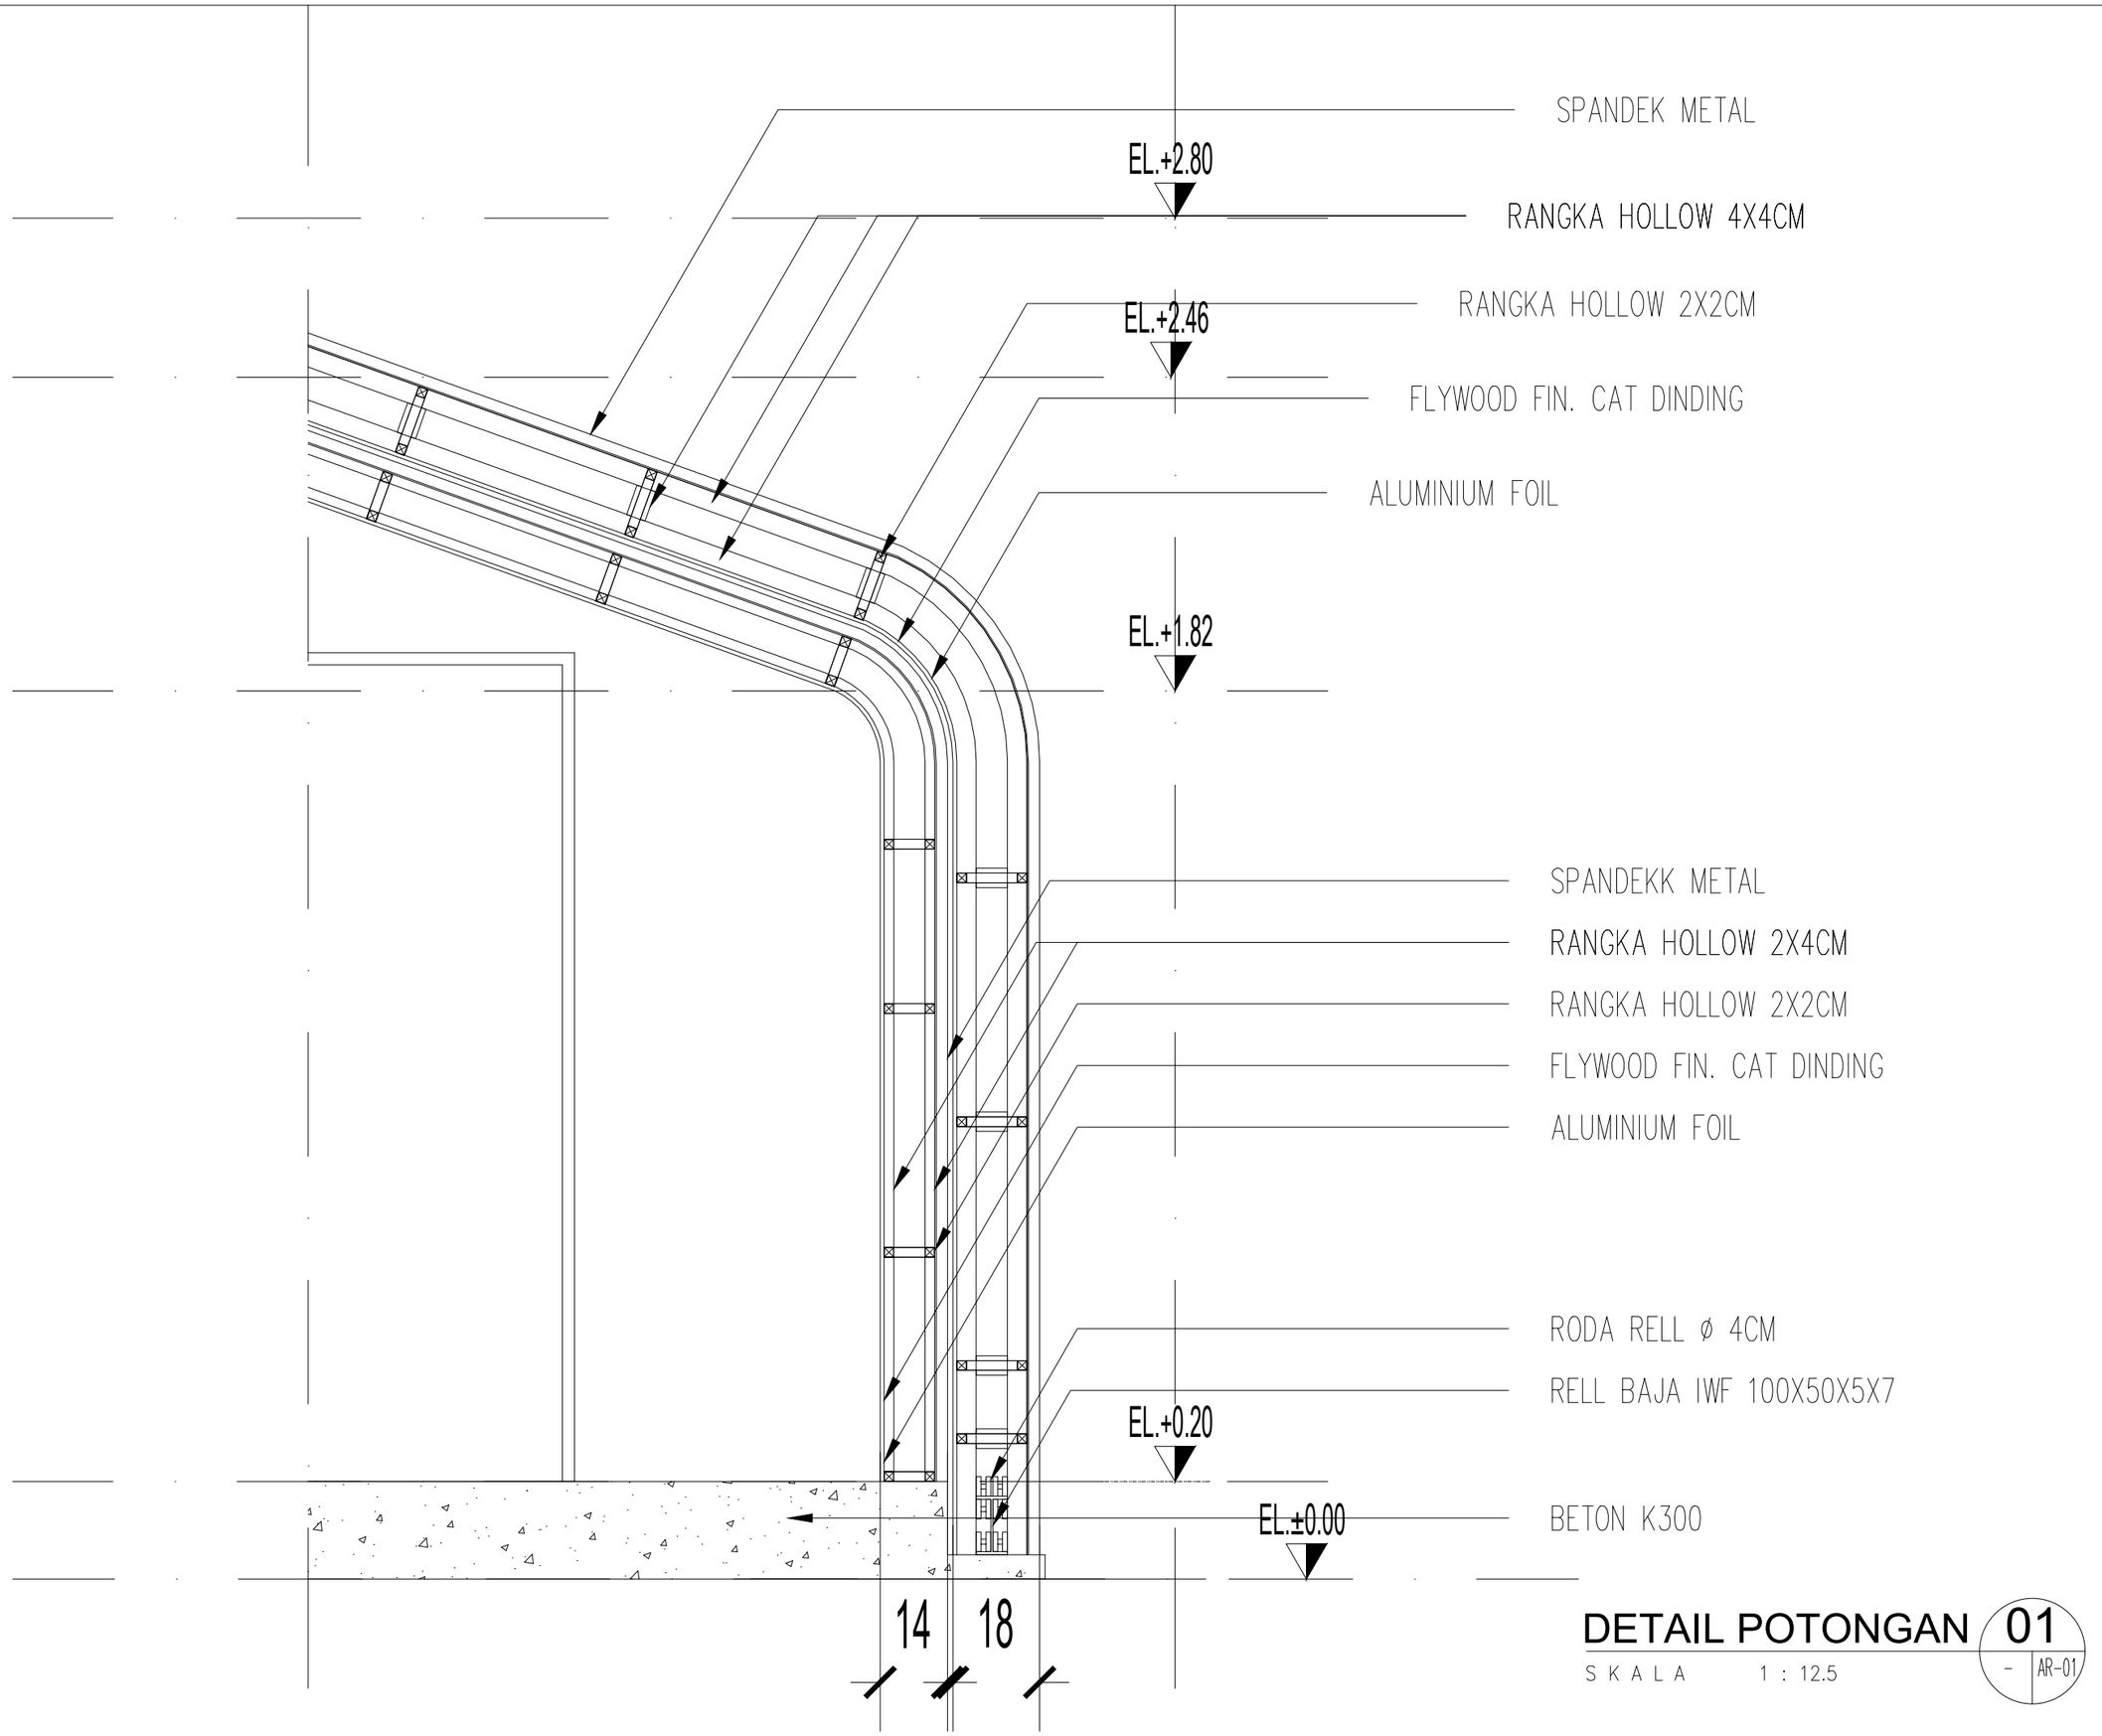

DETAIL POTONGAN 01

SKALA 1 : 12.5

PEMBERI KERJA

CATATAN

REVISI

No.	Rincian	Tanggal	Paraf

PEKERJAAN

DED
OBSERVATORY ROOM

DISETUJUI OLEH

-
-
-

KONSULTAN PERENCANA

PENANGGUNG JAWAB

-
Direktur Utama

TEAM LEADER


-
Team Leader

JUDUL GAMBAR

DETAIL POTONGAN


SKALA	TANGGAL	NO.LEMBAR
1 : 12.5	2026	AR-27

- AR-01

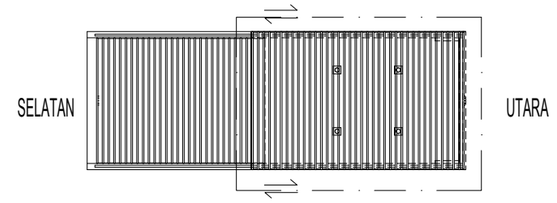

KEYPLAN

SELATAN

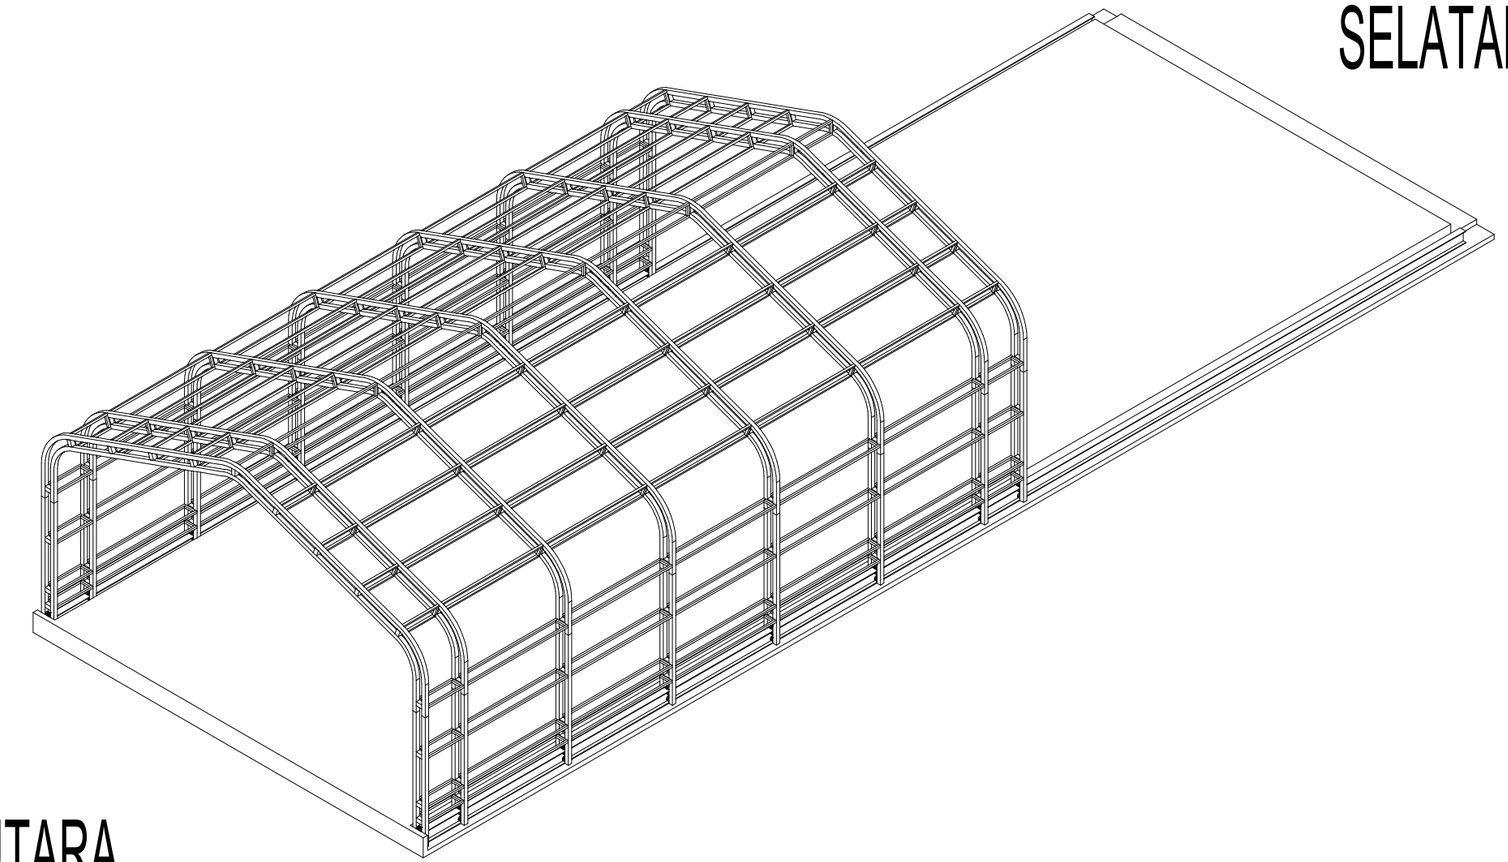

UTARA

ISOMETRIC RANGKA ATAP 1

SKALA 1 : 50

01
- | AR-01

PEMBERI KERJA

CATATAN

REVISI

No.	Rincian	Tanggal	Paraf

PEKERJAAN

DED
OBSERVATORY ROOM

DISETUJUI OLEH

-

-
-

KONSULTAN PERENCANA

PENANGGUNG JAWAB

-
Direktur Utama


TEAM LEADER

-
Team Leader


JUDUL GAMBAR

ISOMETRIC RANGKA ATAP 1

SKALA	TANGGAL	NO.LEMBAR
1 : 50	2026	AR-27

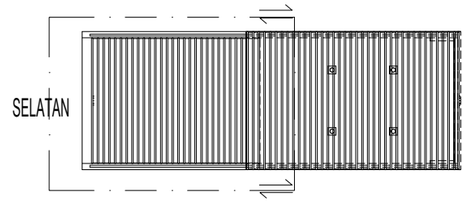

KEYPLAN

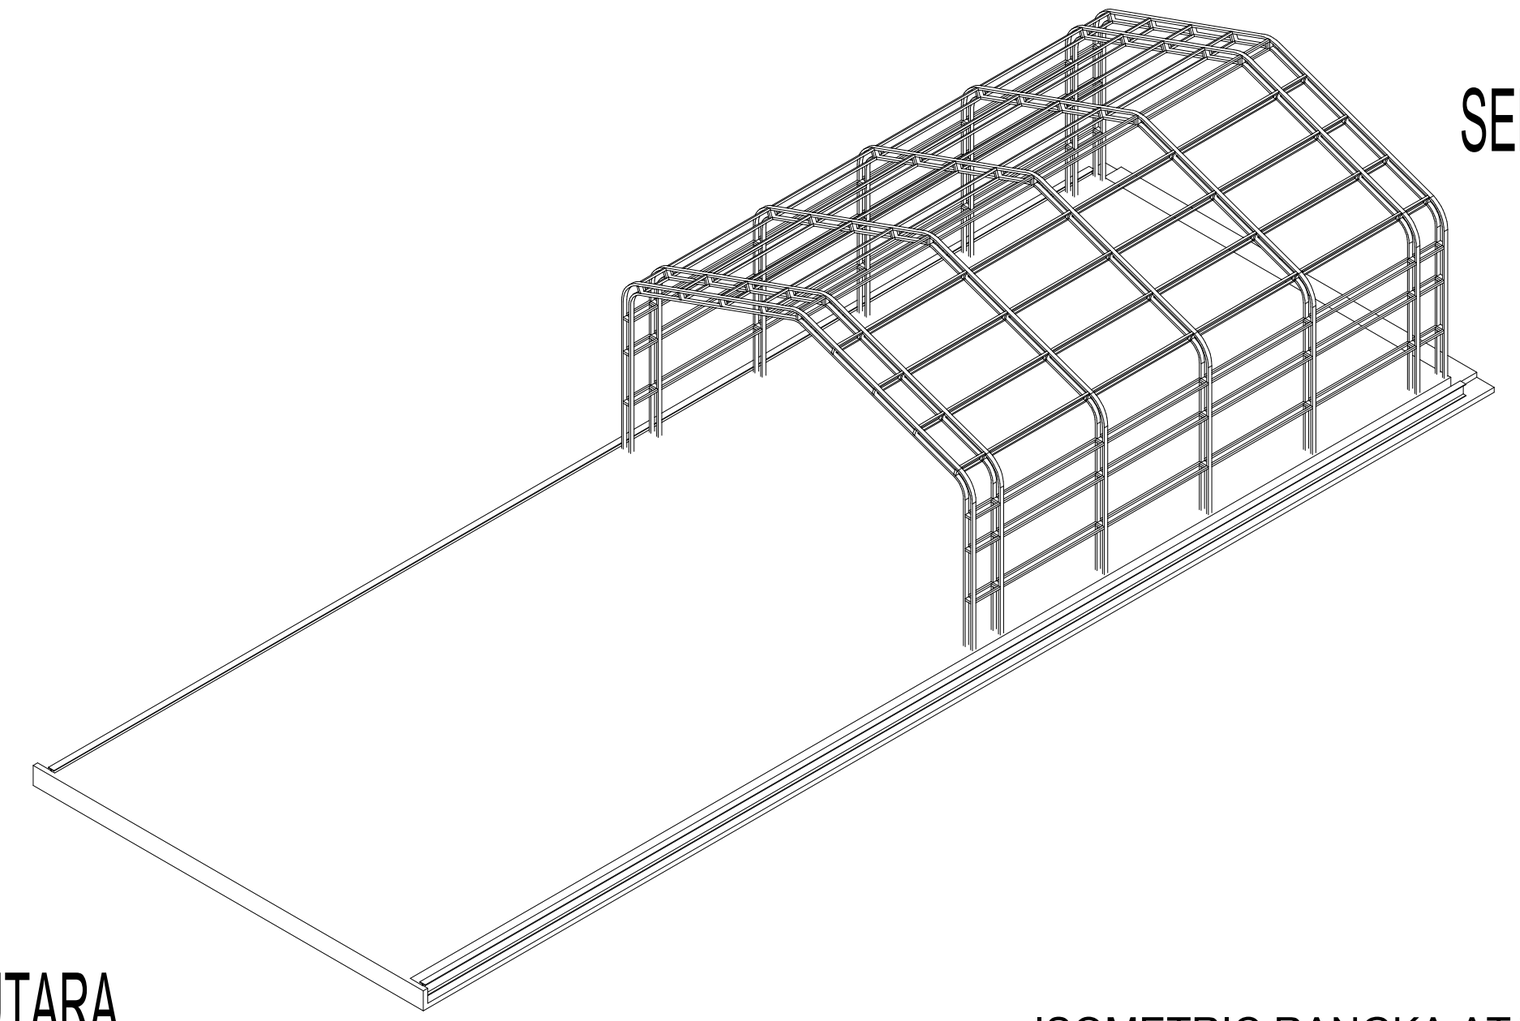

ISOMETRIC RANGKA ATAP 2

SKALA 1 : 50

01 / - / AR-01

PEMBERI KERJA

CATATAN

REVISI

No.	Rincian	Tanggal	Paraf

PEKERJAAN

DED
OBSERVATORY ROOM

DISETUJUI OLEH

-

-
-

KONSULTAN PERENCANA

PENANGGUNG JAWAB

-
Direktur Utama


TEAM LEADER

-
Team Leader

JUDUL GAMBAR

ISOMETRIC RANGKA ATAP 2

SKALA	TANGGAL	NO.LEMBAR
1 : 50	2026	AR-27

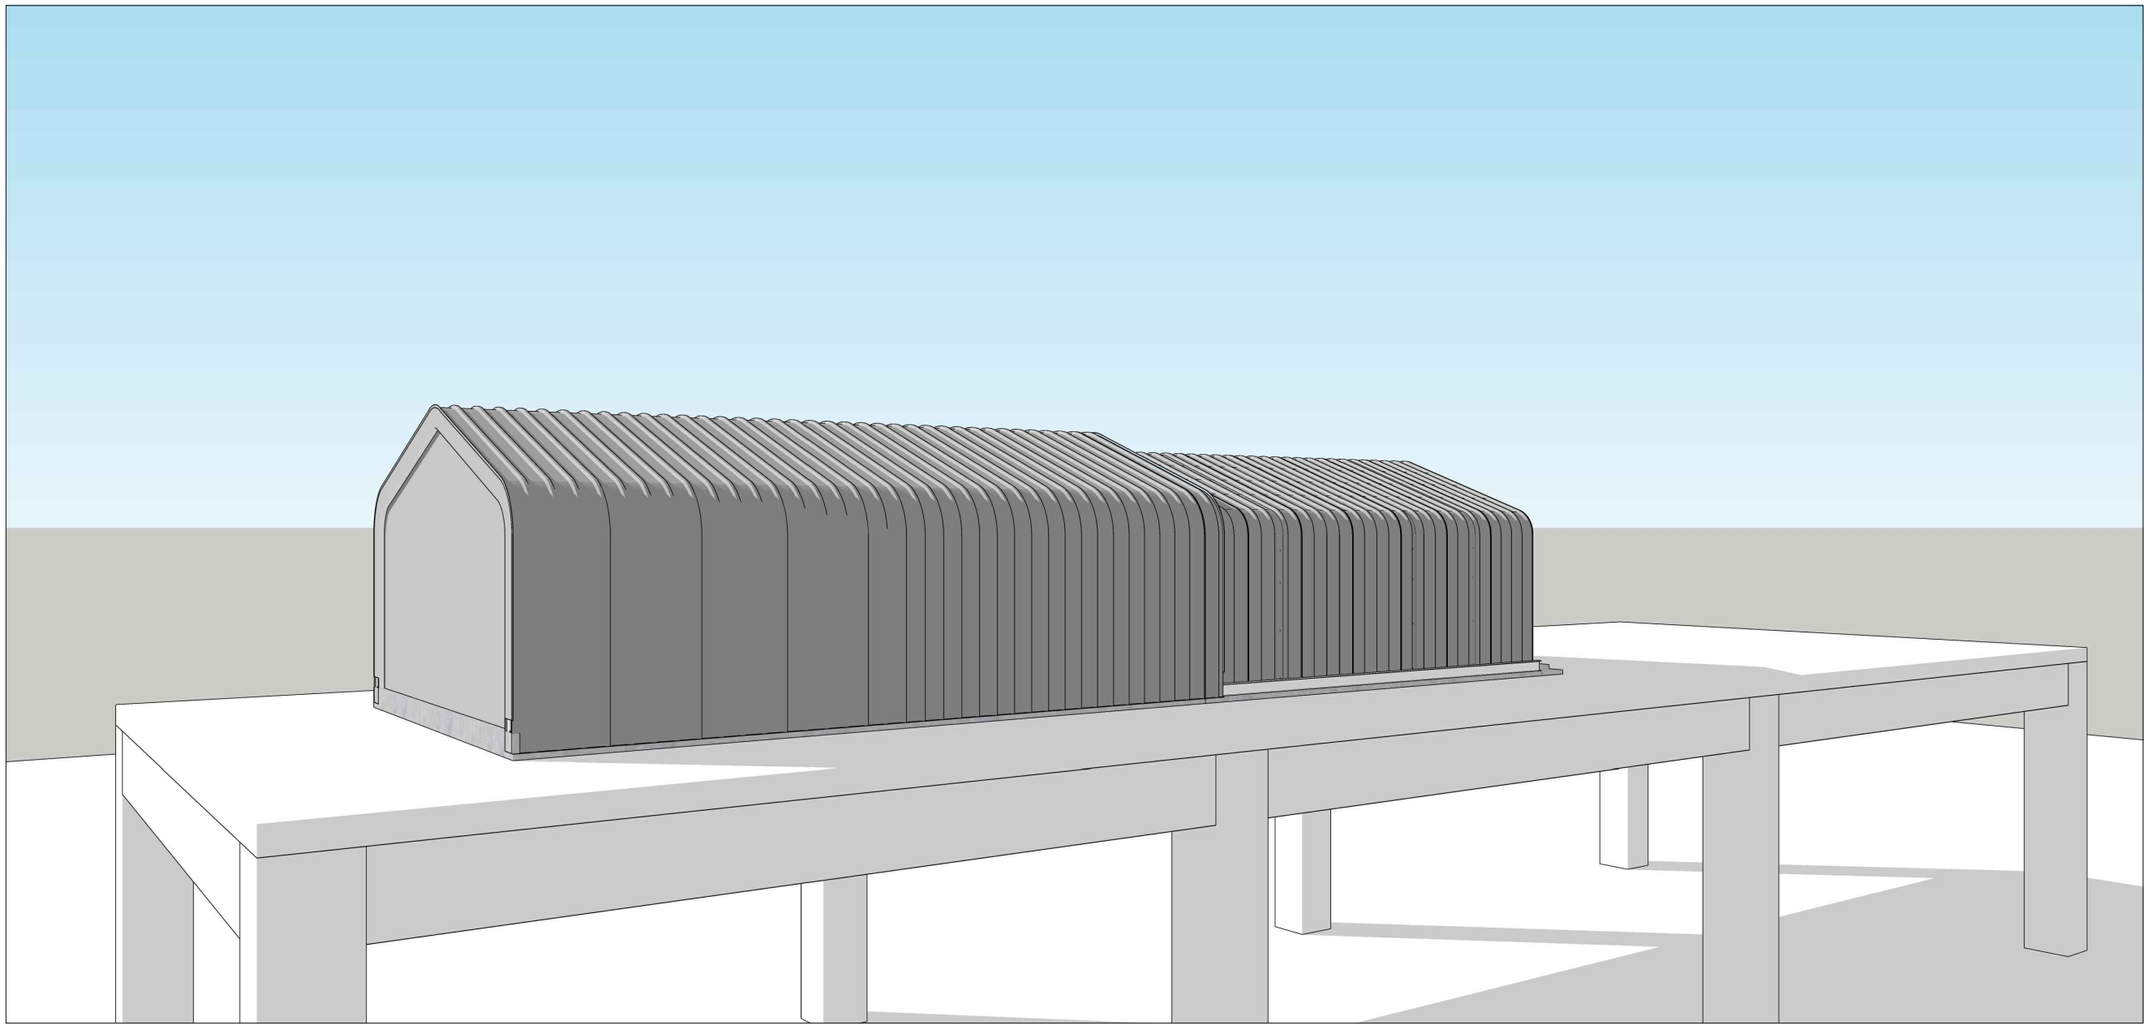

PEMBERI KERJA

CATATAN

REVISI

No.	Rincian	Tanggal	Paraf

PEKERJAAN

DED

OBSERVATORY ROOM

DISETUJUI OLEH

-

-

-

KONSULTAN PERENCANA

PENANGGUNG JAWAB

-

Direktur Utama

TEAM LEADER


-

Team Leader

JUDUL GAMBAR

PERSPEKTIF 1

SKALA	TANGGAL	NO.LEMBAR
1 : 50	2026	AR-27

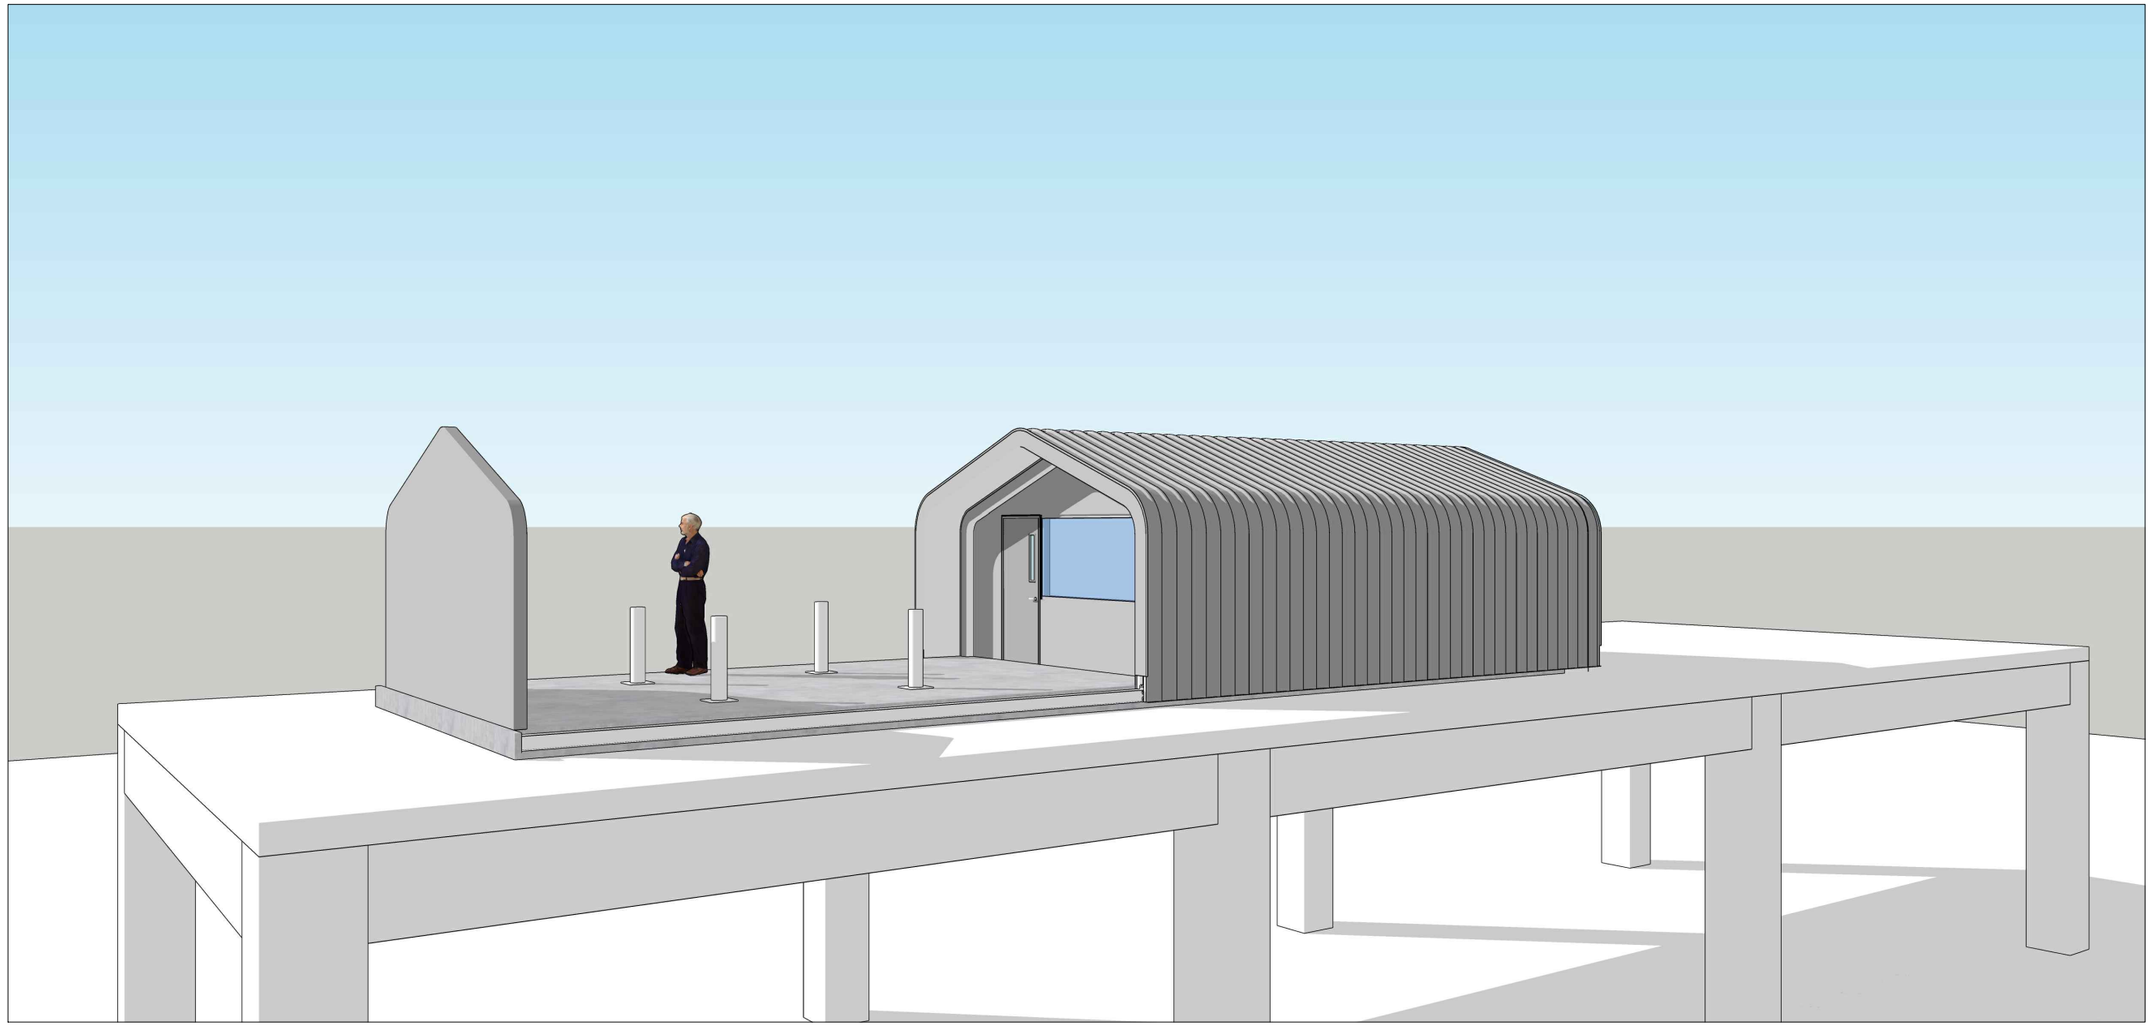

PEMBERI KERJA

CATATAN

REVISI

No.	Rincian	Tanggal	Paraf

PEKERJAAN

DED

OBSERVATORY ROOM

DISETUJUI OLEH

-

-

-

KONSULTAN PERENCANA

PENANGGUNG JAWAB

-

Direktur Utama

TEAM LEADER

-

Team Leader

JUDUL GAMBAR

PERSPEKTIF 2

SKALA	TANGGAL	NO.LEMBAR
1 : 50	2026	AR-27